
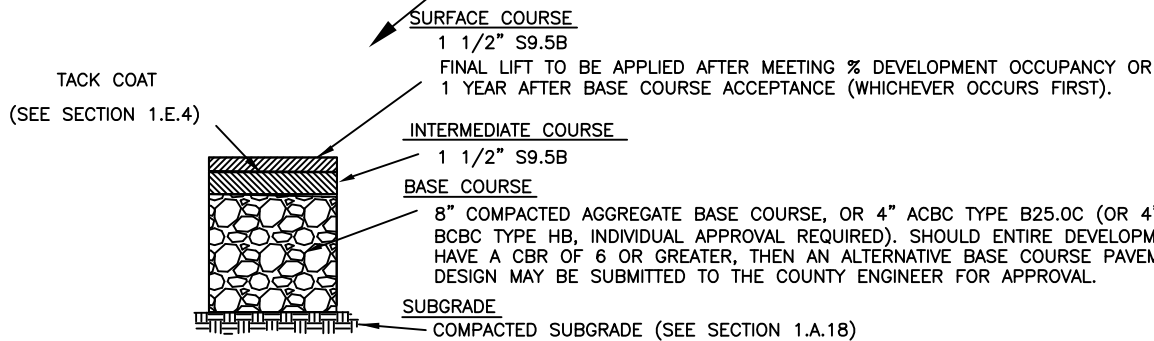


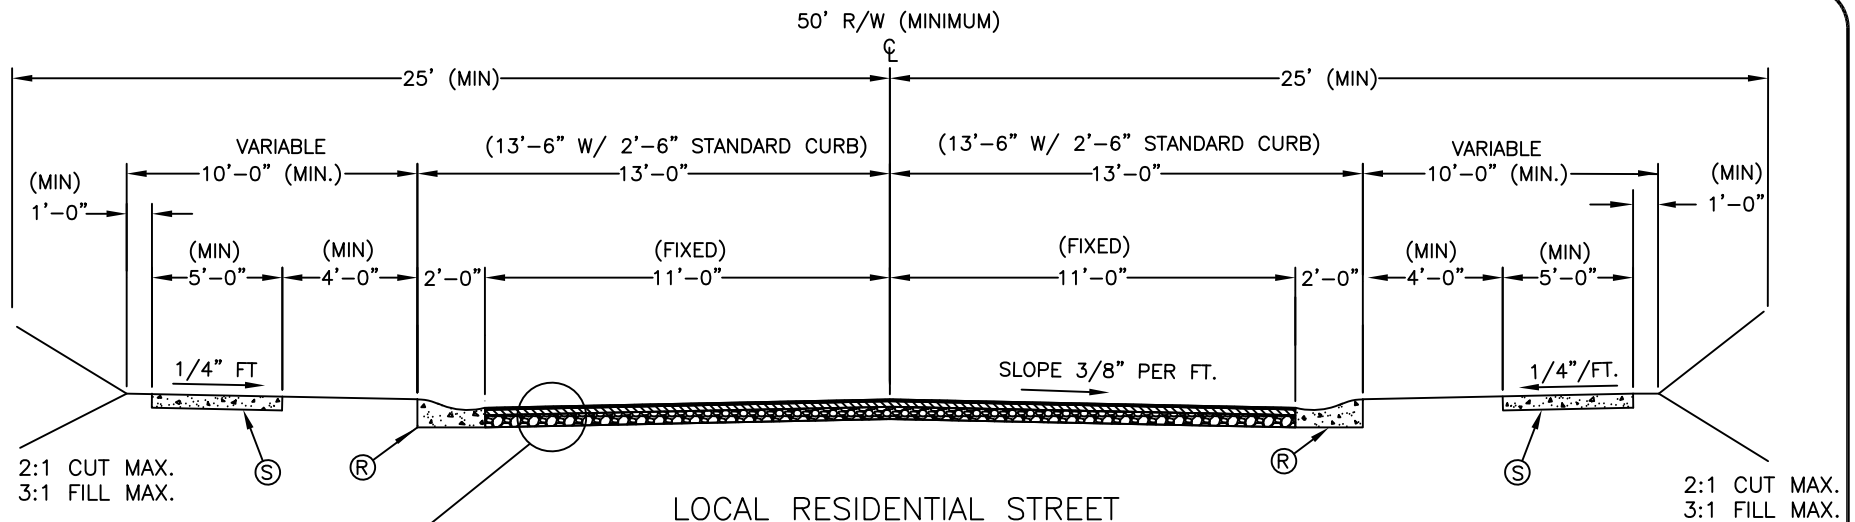

NOTES:

1. SIDEWALK SHALL BE PROVIDED ON BOTH SIDES OF STREET, MINIMUM 4' FROM BACK OF CURB.
2. SEE SECTION 1.F. SIDEWALKS AND DRIVEWAYS.
3. FOR LOCAL RESIDENTIAL STREETS IN THE TOWN OF MATTHEWS, USE DETAIL 11.51.

TYPICAL PAVEMENT SECTION

KEY

- (R) 2'-0" VALLEY GUTTER OR 2'-6" STD. CURB AND GUTTER
- (S) 4" CONCRETE SIDEWALK

REVISIONS

NO.	DATE	DESCRIPTION
1	5/09	REVISED PVMT. SECT.
2	11/16	REVISED SURFACE COURSE AMOUNT
3	9/22	REVISED PAVEMENT MIX TYPES (S9.5B, B25.0C), ADDED NOTE #3

APPROVED DATE: 02/2007

ELEVATION CHANGE AT CENTER LINE REFERENCED FROM TOP OF CURB		
	FOR STONEBASE	FOR ASPHALT
SUBGRADE	- 9-7/8"	- 5-7/8"
BASE COURSE		-1-7/8"
INTERMEDIATE COURSE		-3/8"

MECKLENBURG COUNTY
LAND DEVELOPMENT
STANDARDS



LOCAL RESIDENTIAL STREET TYPICAL SECTION

COMPREHENSIVE STREET CLASSIFICATION SYSTEM (CLASS VI)

STD. NO.	REV.
11.01	3