




APPROVED DATE: 02/2007

NOT TO SCALE

MECKLENBURG COUNTY
LAND DEVELOPMENT
STANDARDS

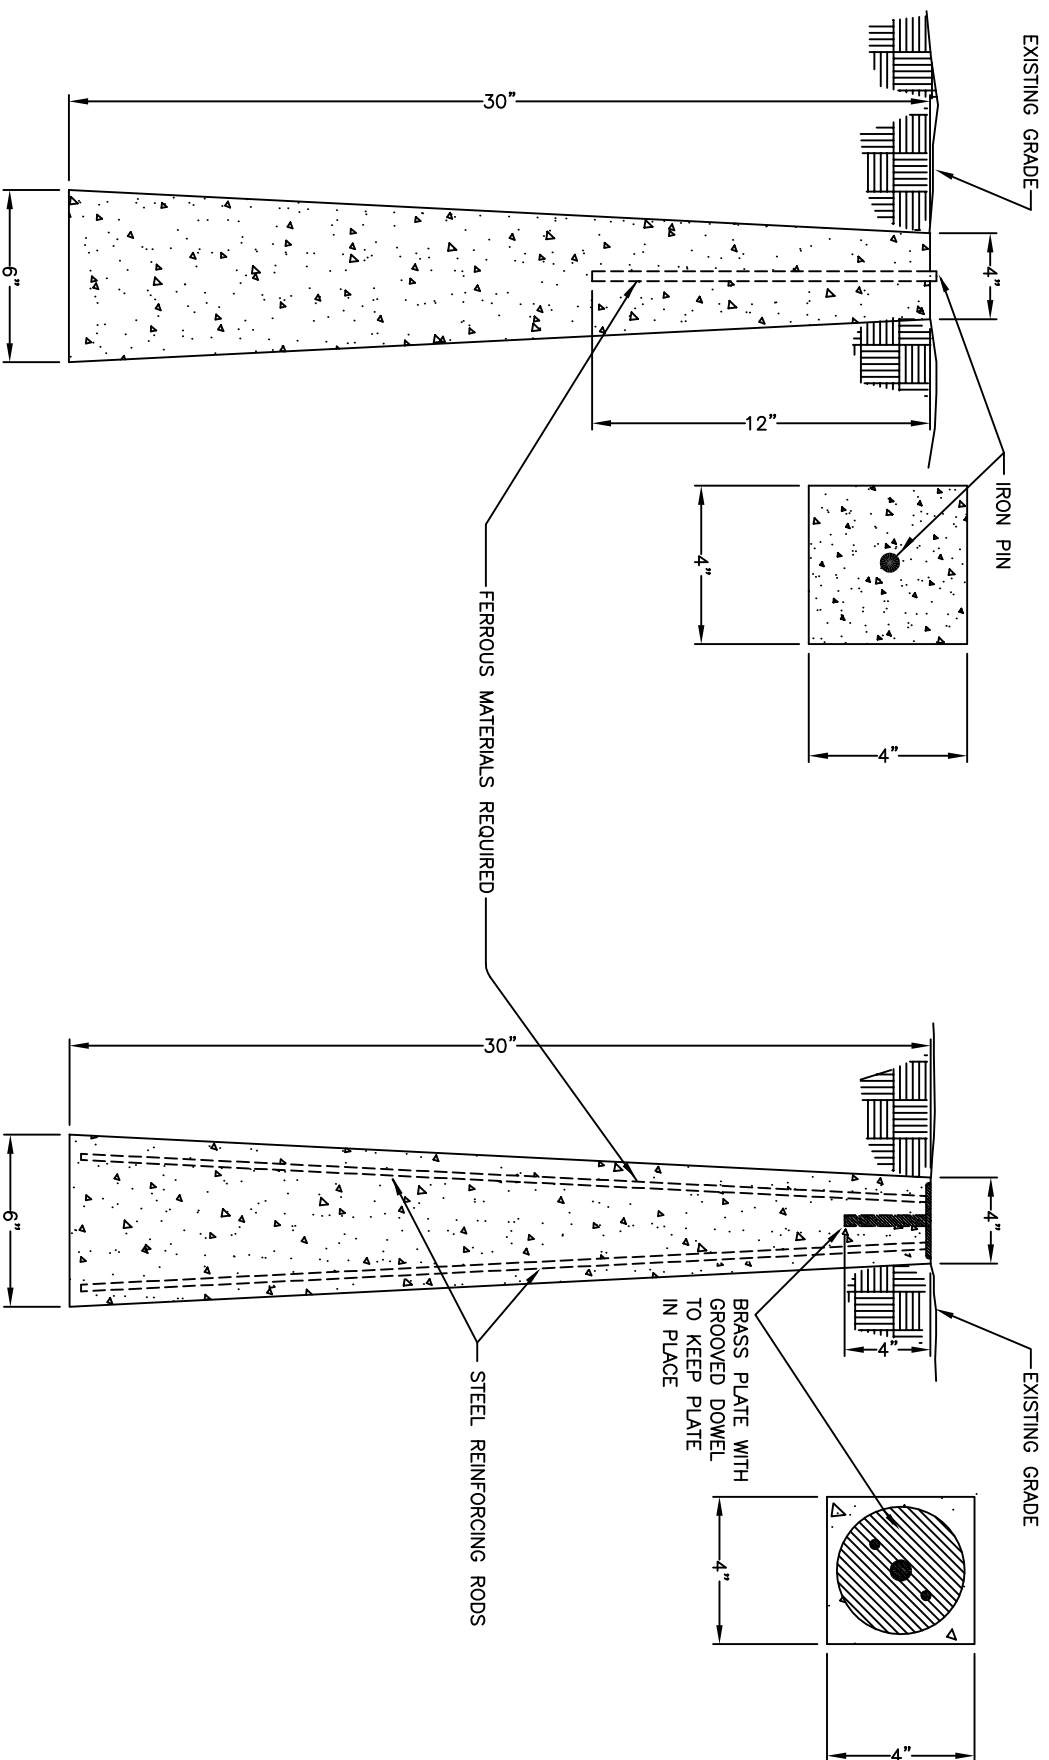

TYPICAL CONCRETE CONTROL MONUMENT

STD. NO.	REV.
50.03	